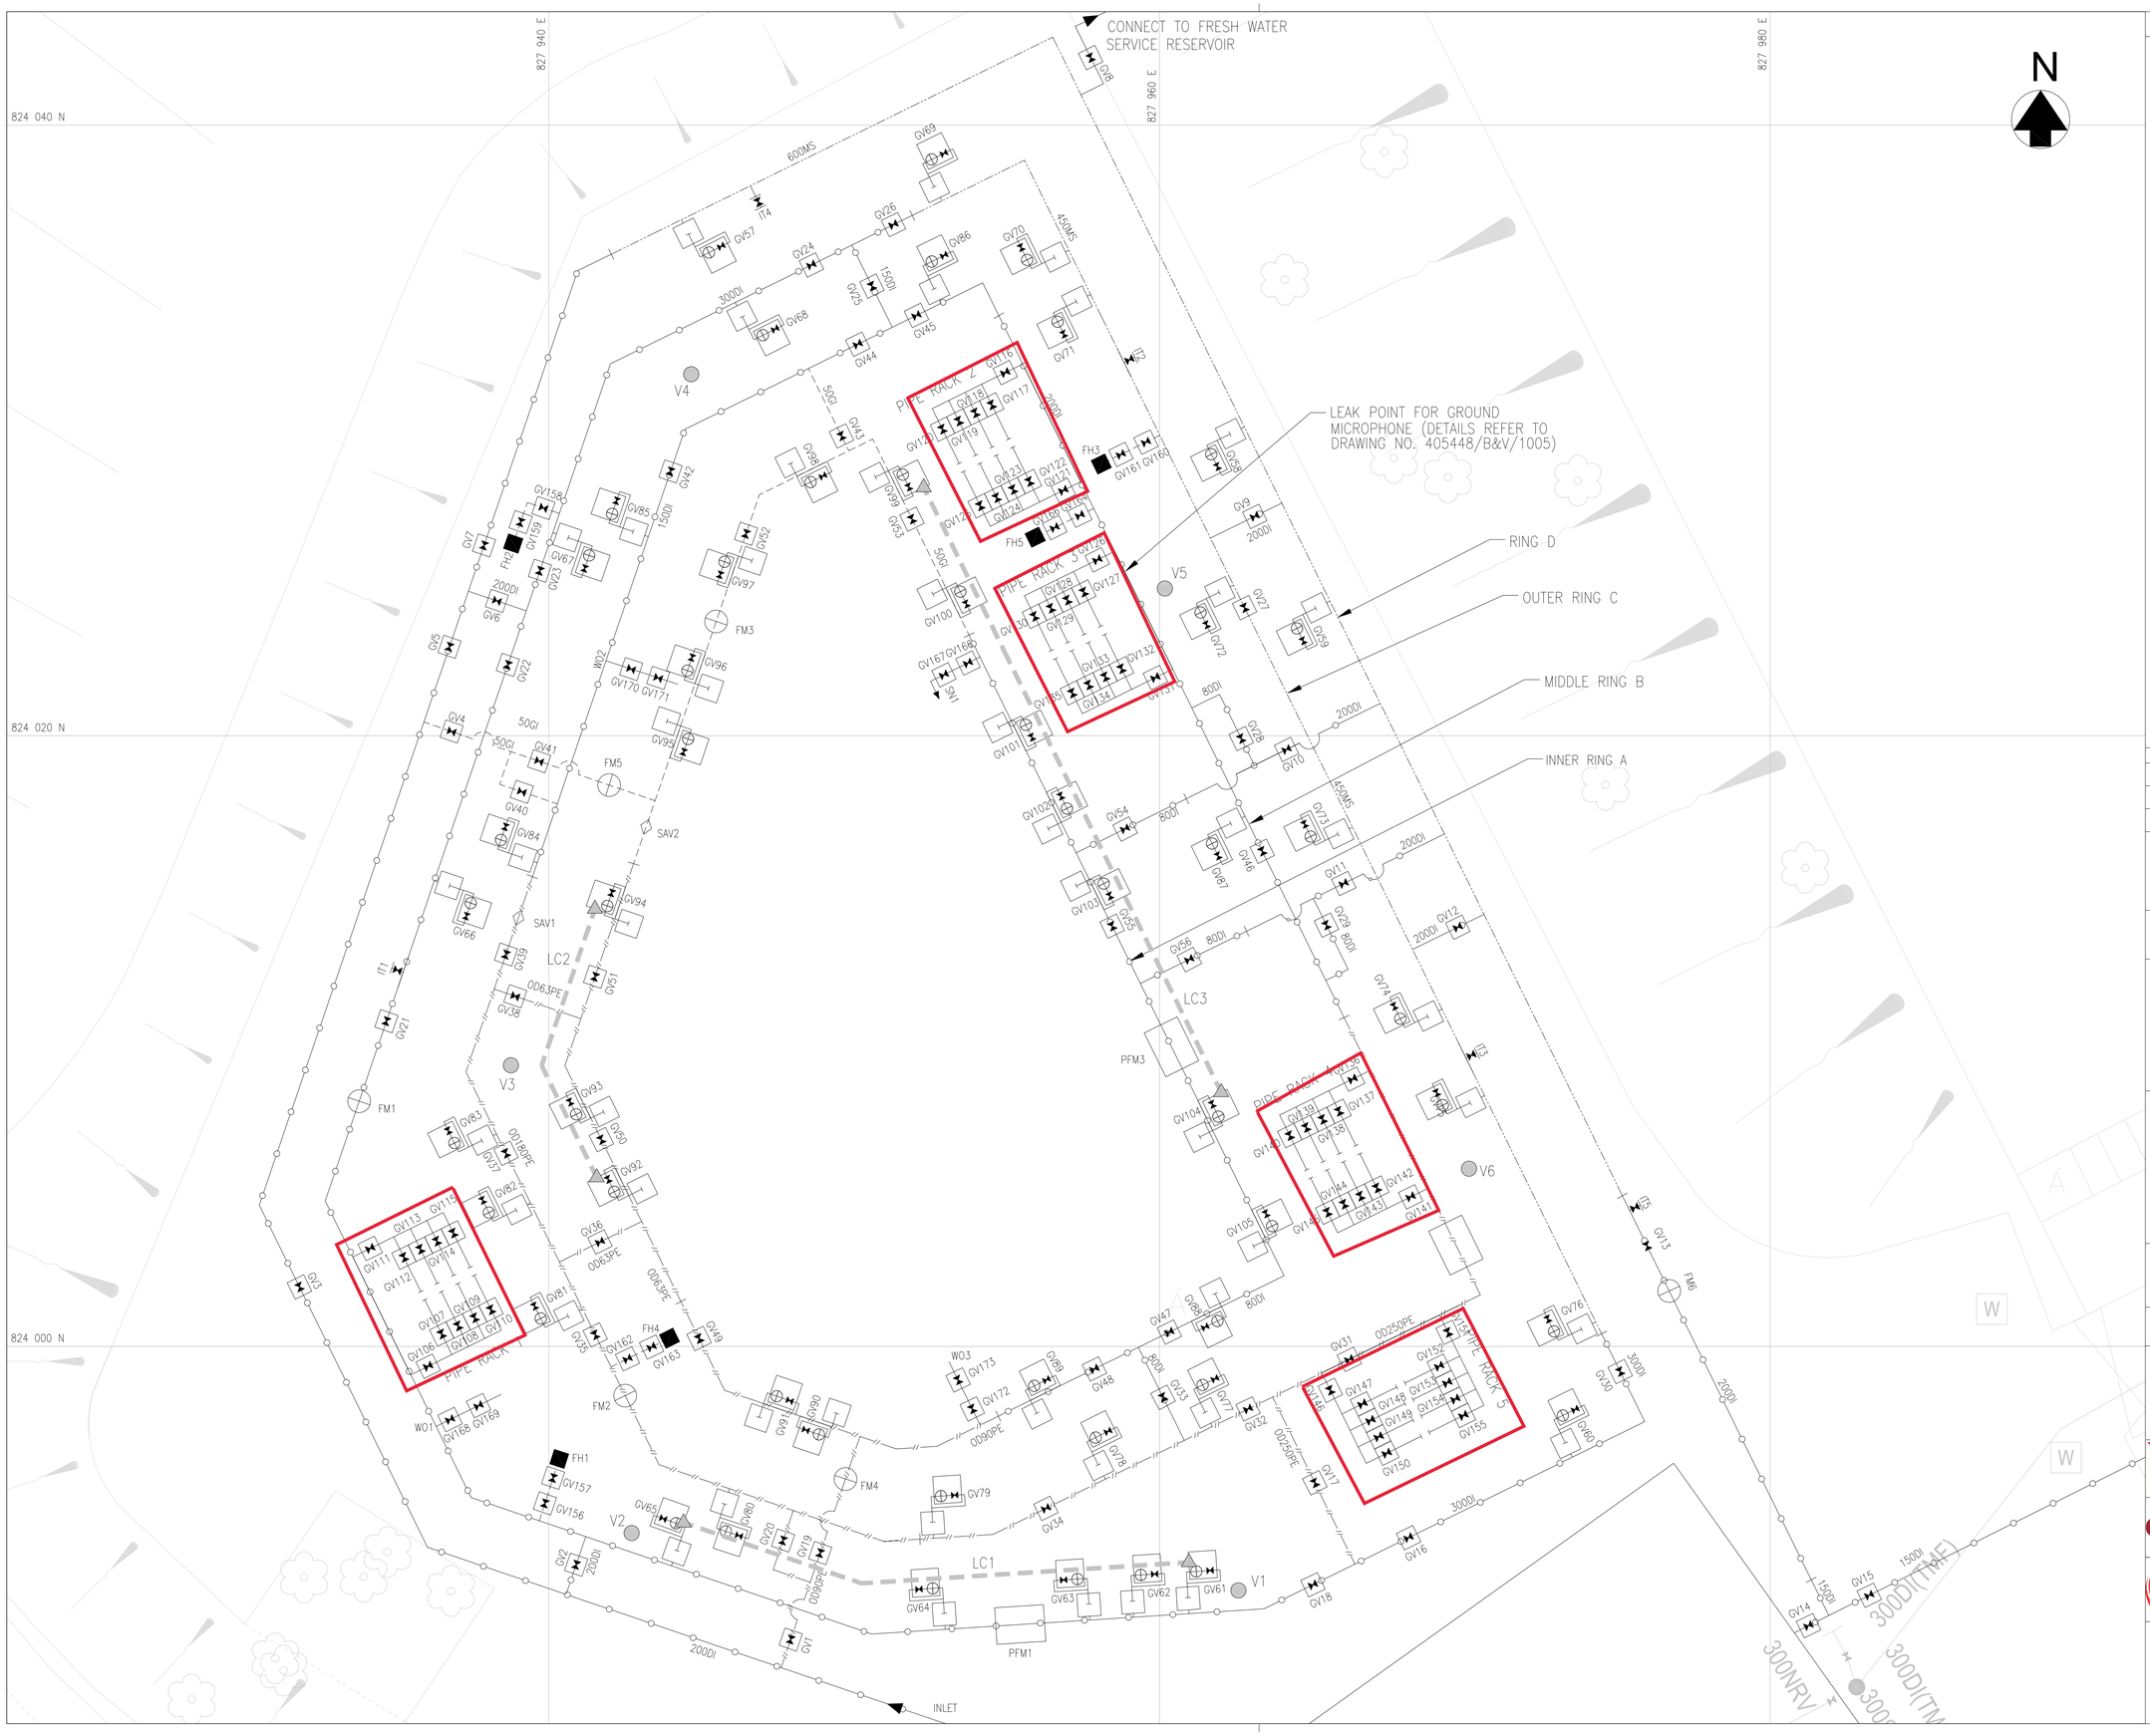

© Copyright by Black & Veatch Hong Kong Limited

LEGEND:

- SINGLE AIR VALVE
- GATE VALVE
- FLOW METER
- DI PIPES
- MS PIPES
- GI PIPES
- PE PIPES
- PORTABLE FLOWMETER CHAMBER
- THRUST BLOCK
- ROUND HEAD FIRE HYDRANT
- WASHOUT
- INSERTION CHAMBER
- SWAN NECK FIRE HYDRANT
- LEAK POINT FOR LEAKAGE NOISE CORRELATOR AND GROUND MICROPHONE (DETAILS REFER TO DRAWING 405448/B&V/1003 & 1004)
- BURIED 1000mm DIA. FIT BALL (DEPTH TO BE DETERMINED ON SITE)
- SINGLE PHASE 5A LIVE CABLE IN 50mm PLASTIC PIPE SLEEVE
- 13A WATER-PROOF POWER SOCKET CONNECTED TO LIGHT BULB OR MINI-GENERATOR

Revision	Date	Description		Initial
	Designed	Checked	Drawn	Checked
Initial	CTAM	FMA	SZ	TL
Date	05/20	05/20	05/20	05/20

Approved

Agreement No.

–

Project Title

CONSULTANCY SERVICE FOR TRAINING DEVELOPMENT OF LEAK DETECTION TRADE

Drawing Title

VALVE SCHEDULE

Drawing No. 405448/B&V/1006

Revision B

Scale A1 1 : 100
A3 1 : 200

水務署
Water Supplies Department

PolyU Technology and Consultancy Company Limited 理大科技及顧問有限公司

THE HONG KONG POLYTECHNIC UNIVERSITY 香港理工大學

DEPARTMENT OF LAND SURVEYING AND GEO-INFORMATICS 土地測量及地理資訊學系

BLACK & VEATCH HONG KONG LIMITED 博威工程顧問有限公司

Y:\Daily Work\2020\1117\405448-B&V-1006.dwg, 11/17/2020 4:43:15 PM, Bluebeam PDF